
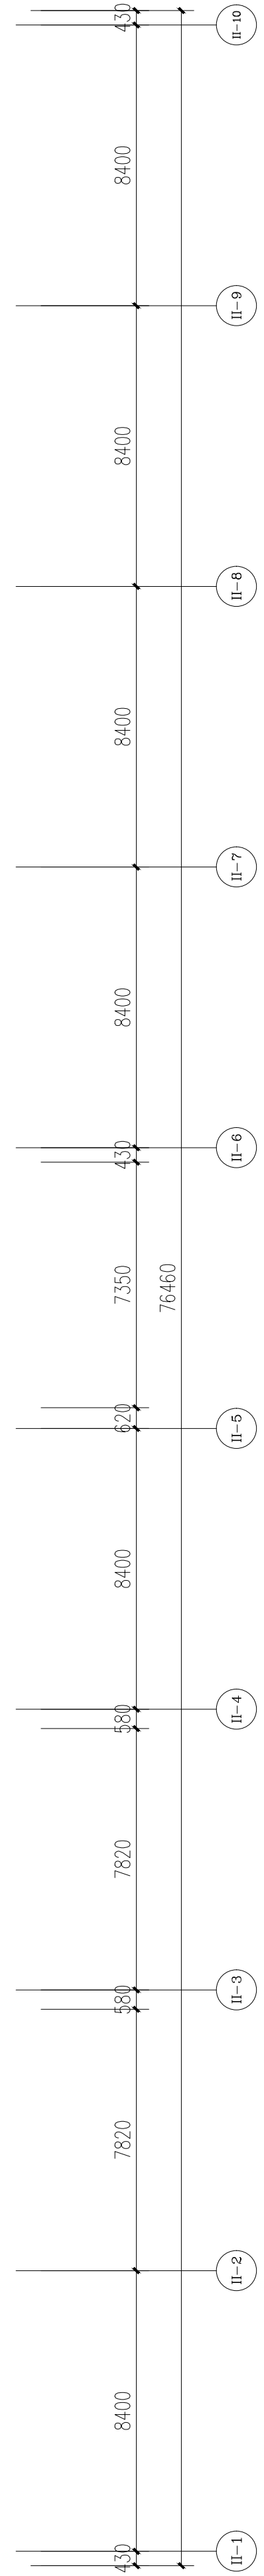


1:300

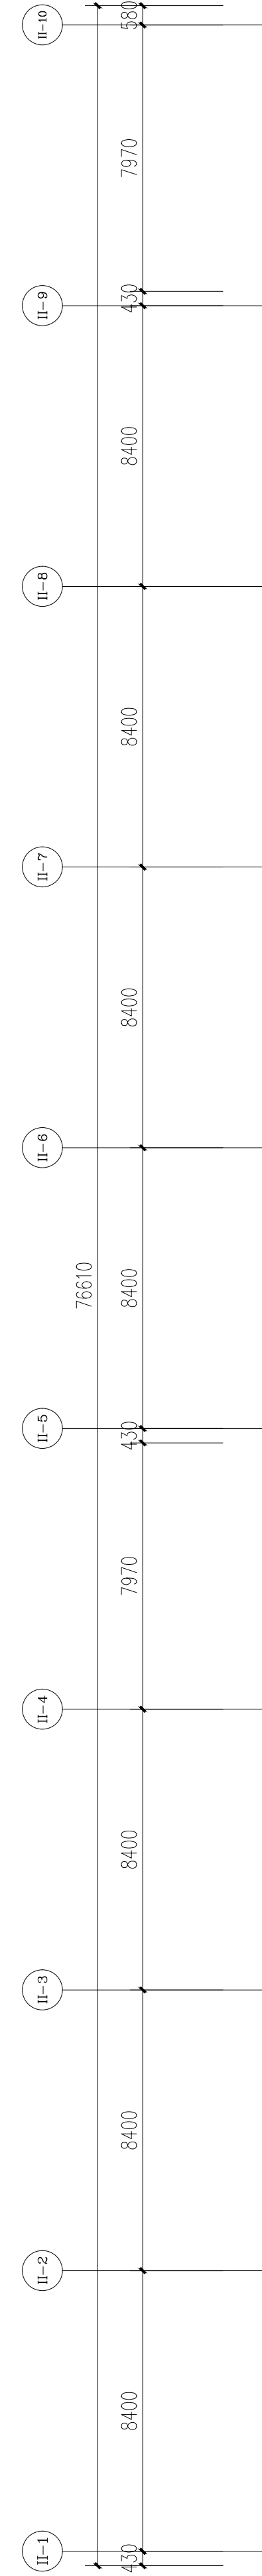

BIAD
北京市建筑设计研究院股份有限公司
Beijing Institute of Architectural Design Co., Ltd.

中国 北京 南礼士路62号 100845
NO.62 NANLISHI ROAD, BEIJING, P.R.CHINA
POSTCODE: 100845
TEL: 86-10-88021578
FAX: 86-10-88021570
WEBSITE: WWW.BIAD.COM.CN

本图权的著作权及图形版权归北京中
建设计研究院股份有限公司 (BIAD) 所有。
图中所有的内容设计信息均由子图提供。本图及分
子图均受法律保护。未经许可复制或传播本图或
其内容均属侵权行为。本公司与客户另有约定的
除外。 (以下)

This drawing is the property of BIAD and is not to be
reproduced or copied in whole or in part.
It is only to be used for the project and site specifically
identified herein and is not to be used on any other
project.
Drawing with BIAD seal are the official version for
construction.

专业设计部门 DEPARTMENT

设计签字
SIGNATURE

方案设计人 DESIGNER DESIGNER	
设计负责人 DESIGNER DESIGNER	
专业负责人 SPECIALIST SPECIALIST	
设计人 DESIGNER DESIGNER	

验证签字
VERIFICATION

审核人 CHECKER CHECKER	
审定人 APPROVED APPROVED	

会签
CONFIRMATION

建筑专业负责人 ARCHITECT	
结构专业负责人 STRUCTURE	
给排水专业负责人 PLUMB	
暖通空调专业负责人 HVAC	
电气专业负责人 ELECTRIC	

项目名称 PROJECT NAME

项目编号 PROJECT NO.

图名 DRAWING NAME

设计阶段 PHASE	图号 DRAWING NO.	版本号 VERSION
---------------	-------------------	----------------

出图日期 DATE	年 YEAR	月 MONTH	日 DAY
--------------	-----------	------------	----------

修改记录
MODIFICATION