
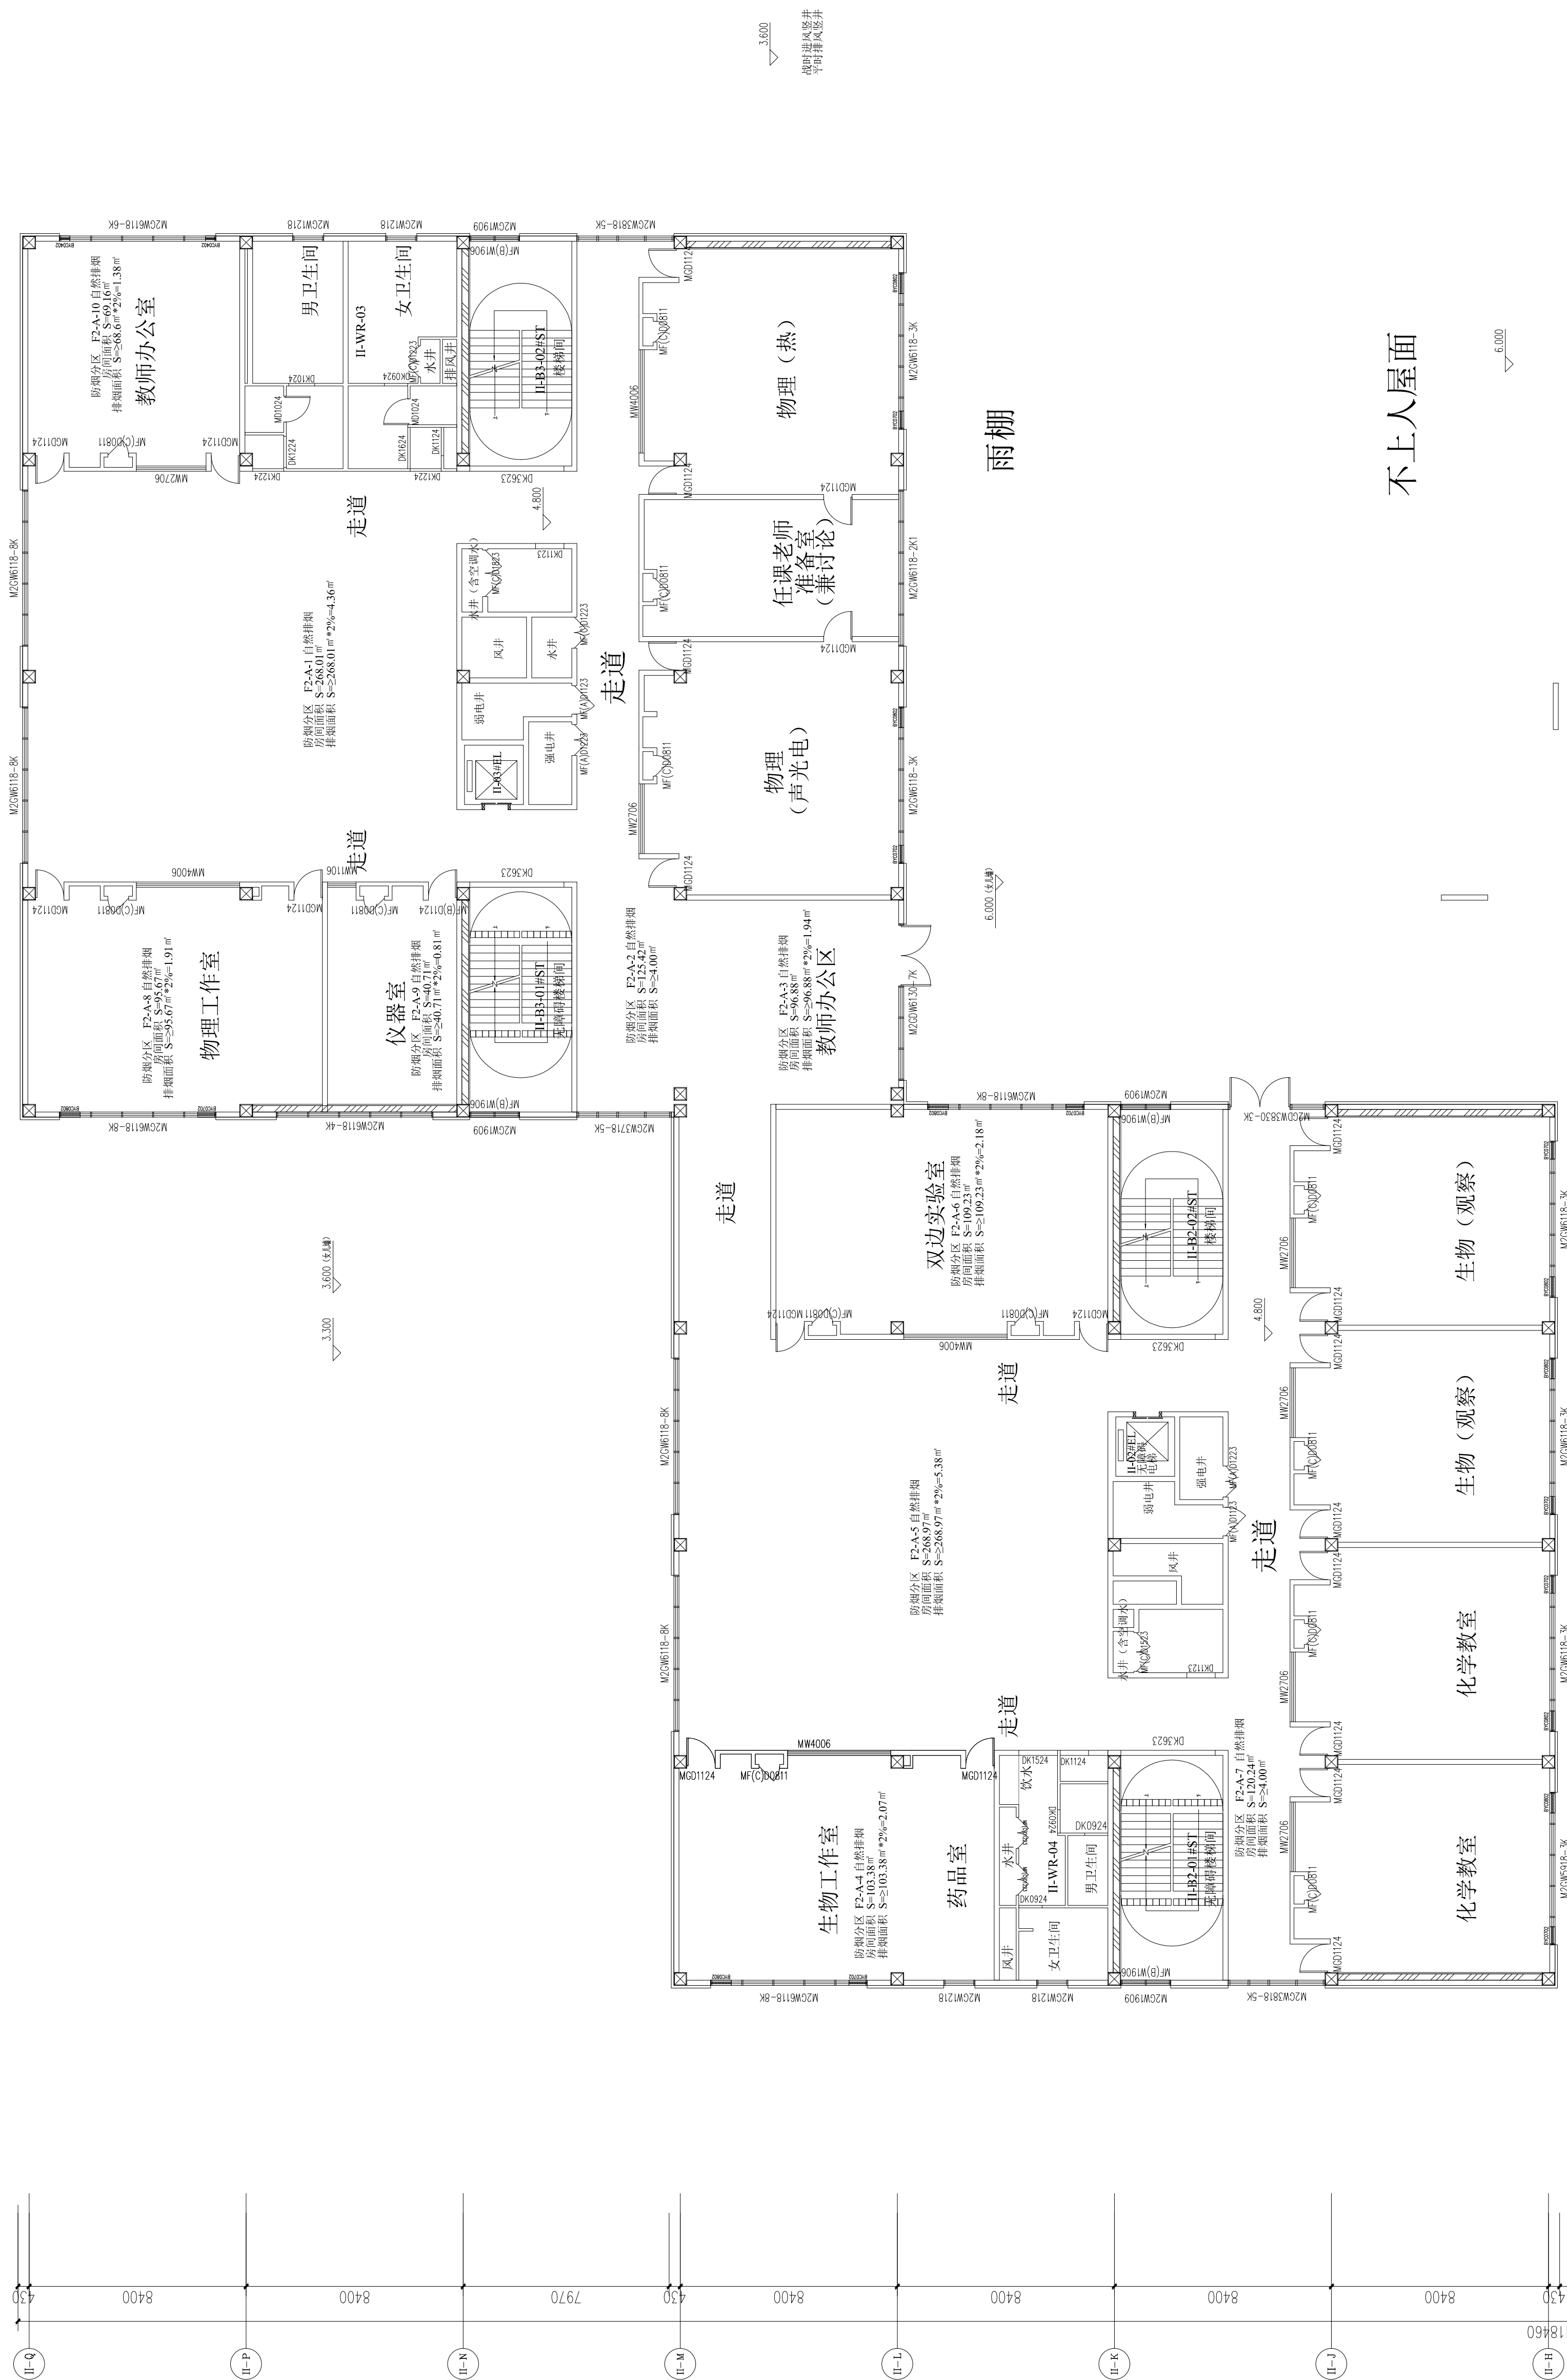
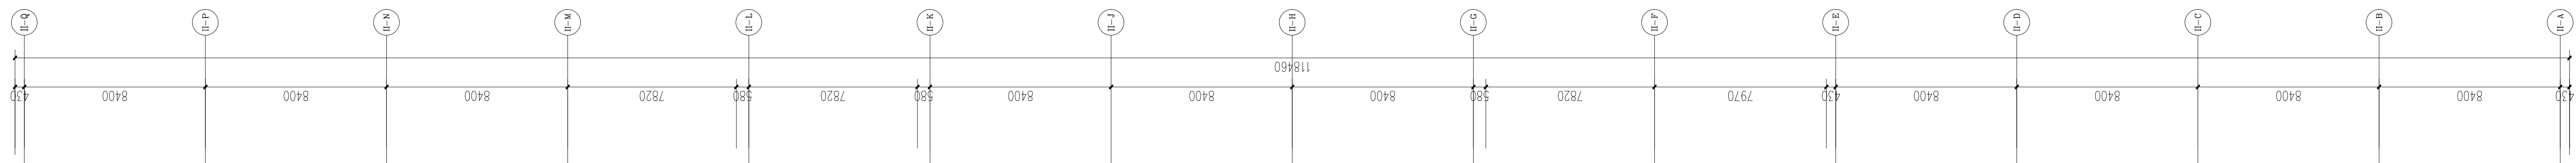


1:300

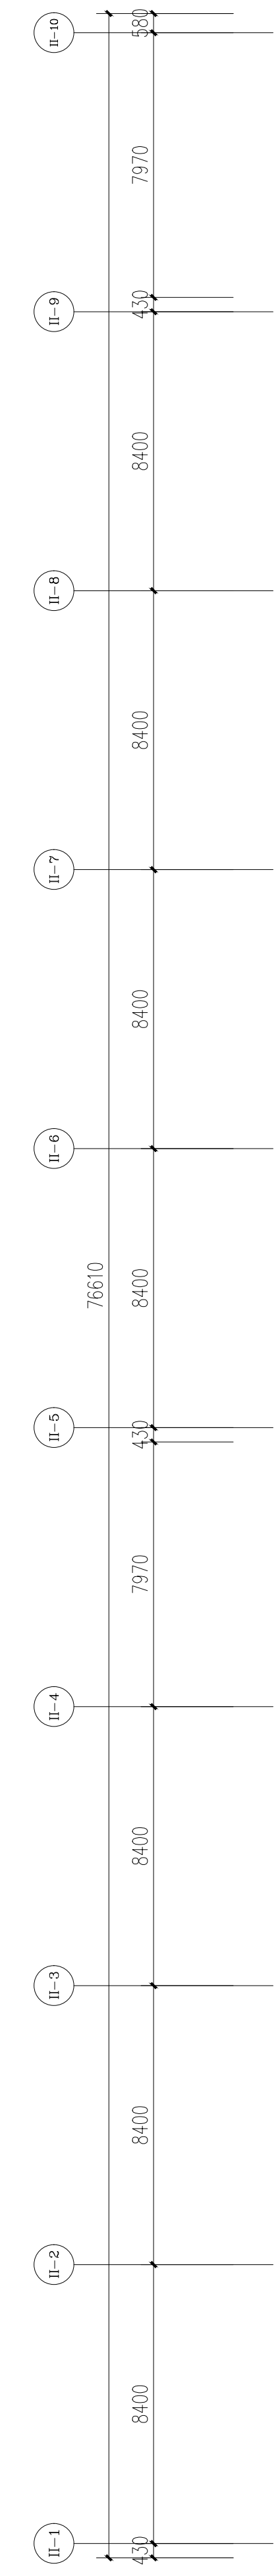



屋顶平台 (上人)

最大活动人数160人

雨棚

不上人屋面

雨棚

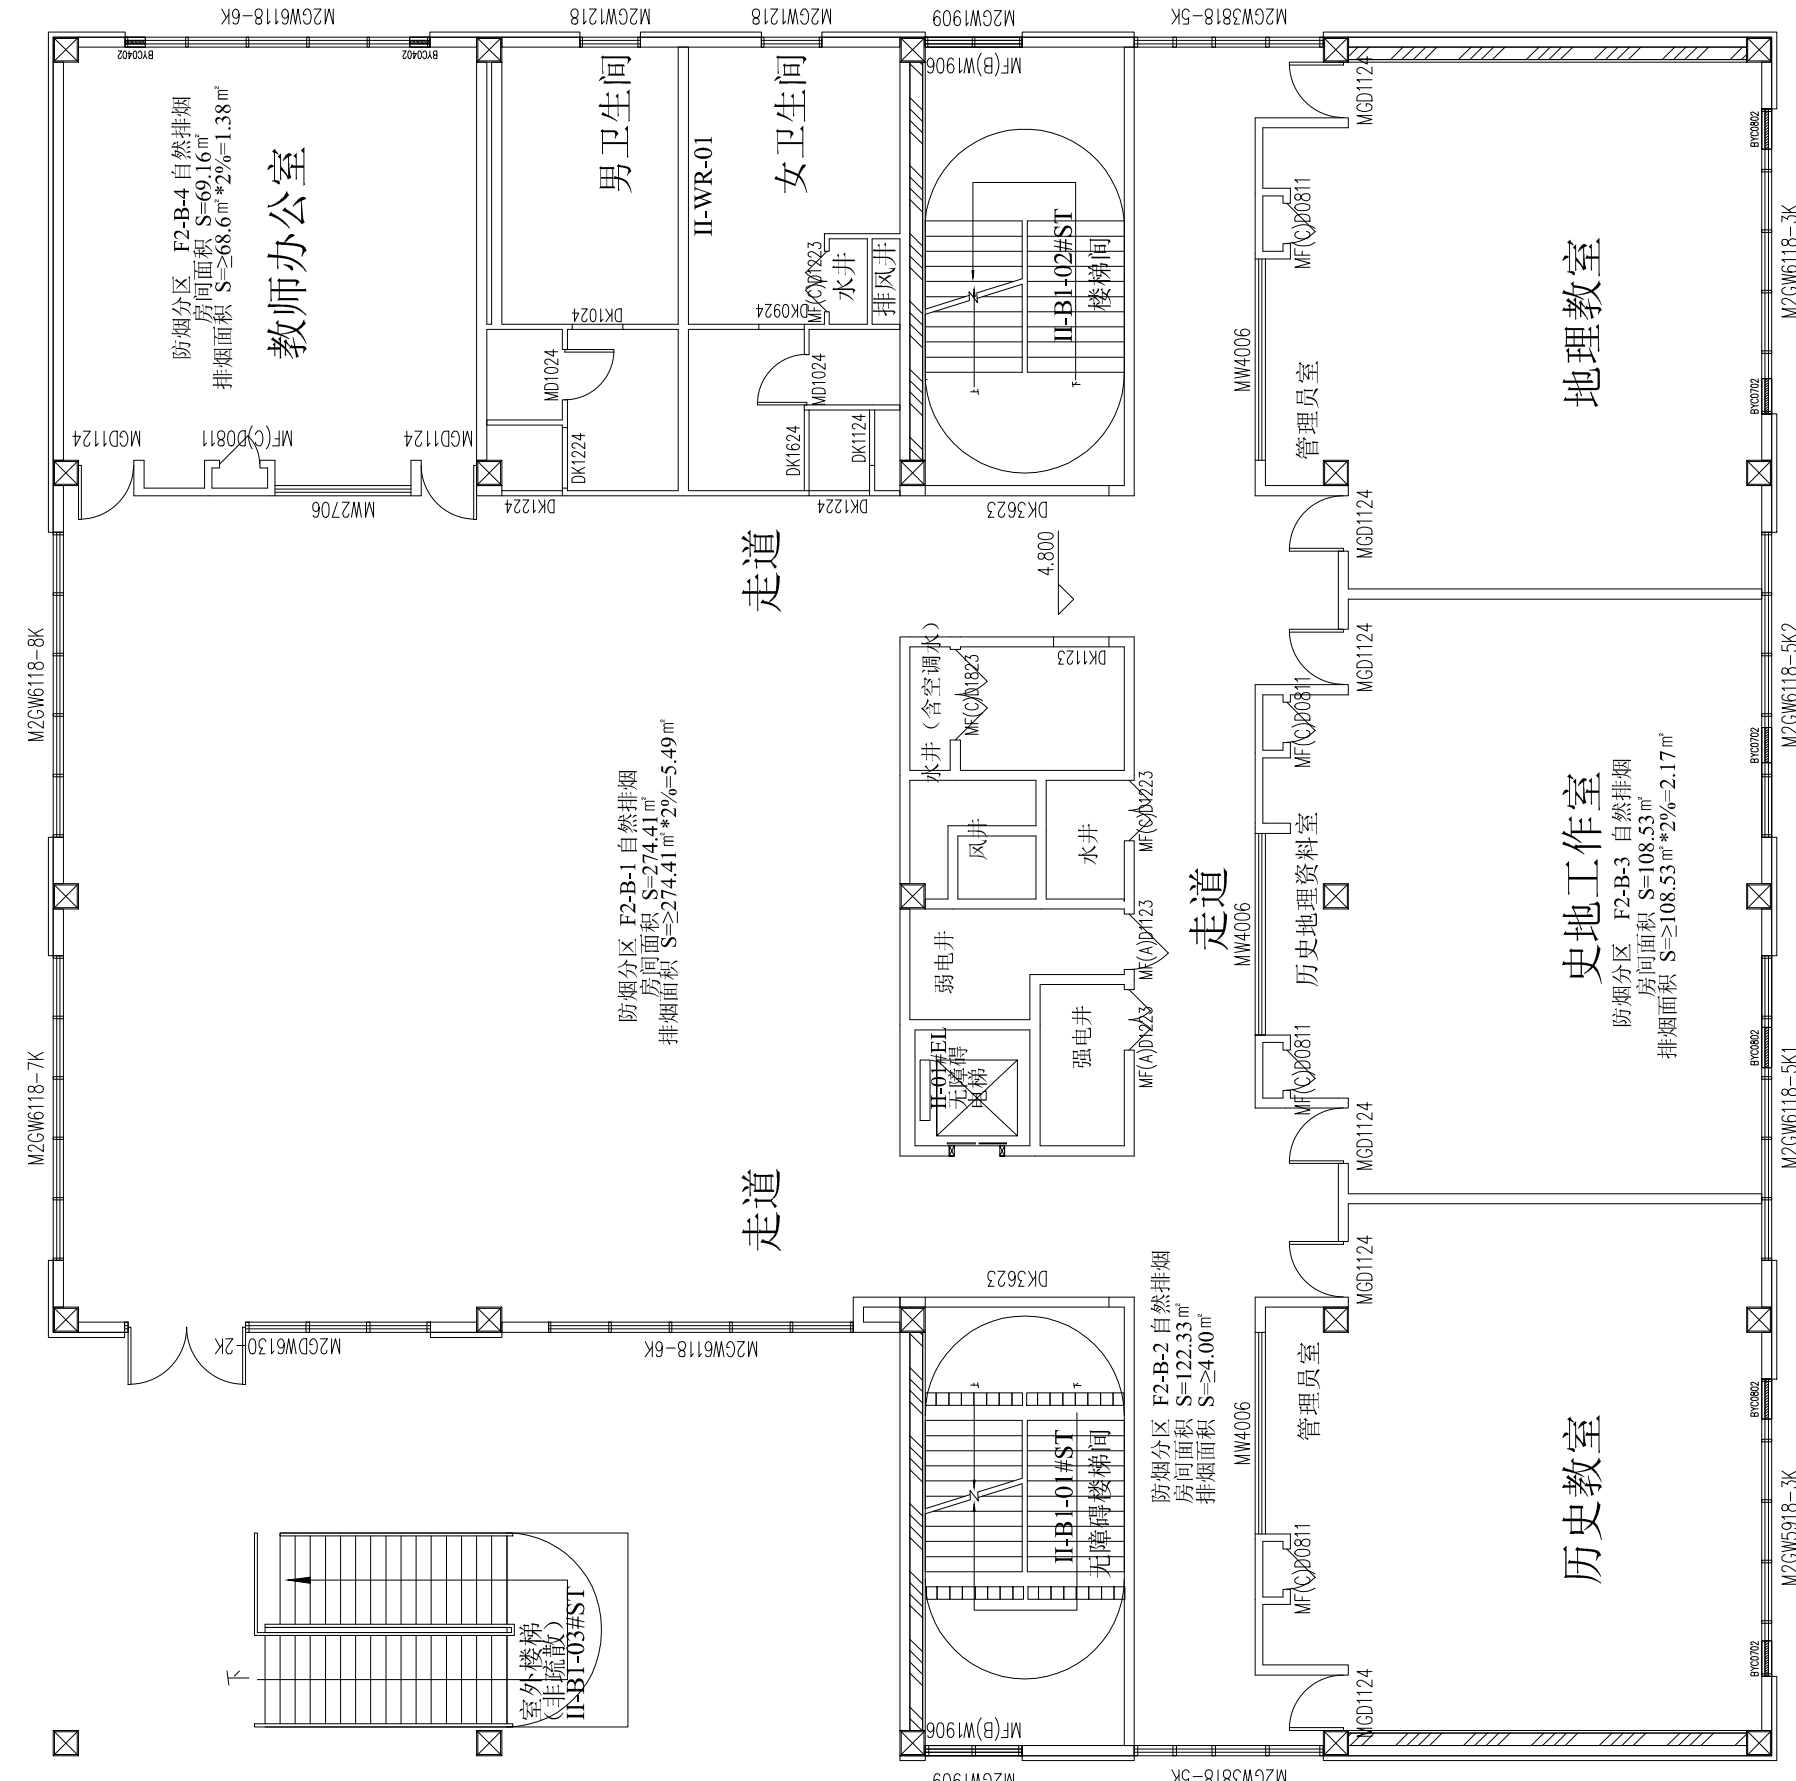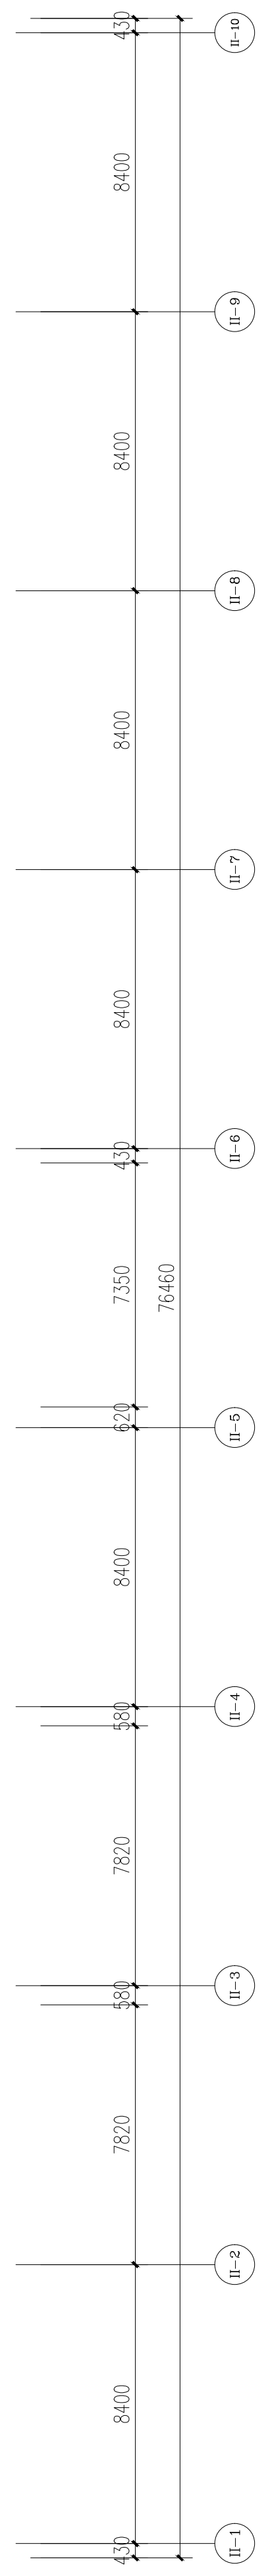

BIAD

北京市建筑设计研究院股份有限公司

BEIJING INSTITUTE OF ARCHITECTURAL DESIGN CO.,LTD.

中国 北京 南礼士路62号 100845

NO.62 NANLISHI ROAD, BEIJING, P.R.CHINA

POSTCODE: 100845

TEL: 86-10-88021576

FAX: 86-10-88021570

WEBSITE: WWW.BIAD.COM.CN

本图形的著作权及图形版权归北京中

建院设计研究院股份有限公司 (BIAD) 所有。

图中所有的手写标注及信息均由手提供。本图及本

公司所有。不得复制或翻印。如有复制或翻印

或擅自修改者, 本公司与客户另行约定, 或

追究其法律责任。

加盖有文件章的图形为BIAD正式文件之施

工图。

This drawing is the property of BIAD and is not to be

reproduced or copied in whole or in part.

It is only to be used for the project and site specifically

identified herein and is not to be used on any other

project.

Designs with BIAD seal are the official version for

construction

专业设计部门

DEPARTMENT

设计签字

SIGNATURE

方案设计师

DESIGNER

方案审核人

DESIGNER

设计负责人

DESIGNER

专业负责人

DESIGNER

设计人

DESIGNER

验证签字

VERIFICATION

审核人

CHECKER

审核人

CHECKER

会签

CONFIRMATION

建筑专业负责人

ARCHITECT

结构专业负责人

STRUCTURE

给排水专业负责人

PLUMBING

暖通空调专业负责人

HEATING

电气专业负责人

ELECTRIC

项目名称

PROJECT NAME

项目编号

PROJECT NO.

图名

SHOWING NAME

设计阶段

PHASE

图号

DRAWING NO.

版本号

VERSION

出图日期

DATE

年

月

日

DATE

MONTH

DAY

修改记录

MODIFY RECORD