


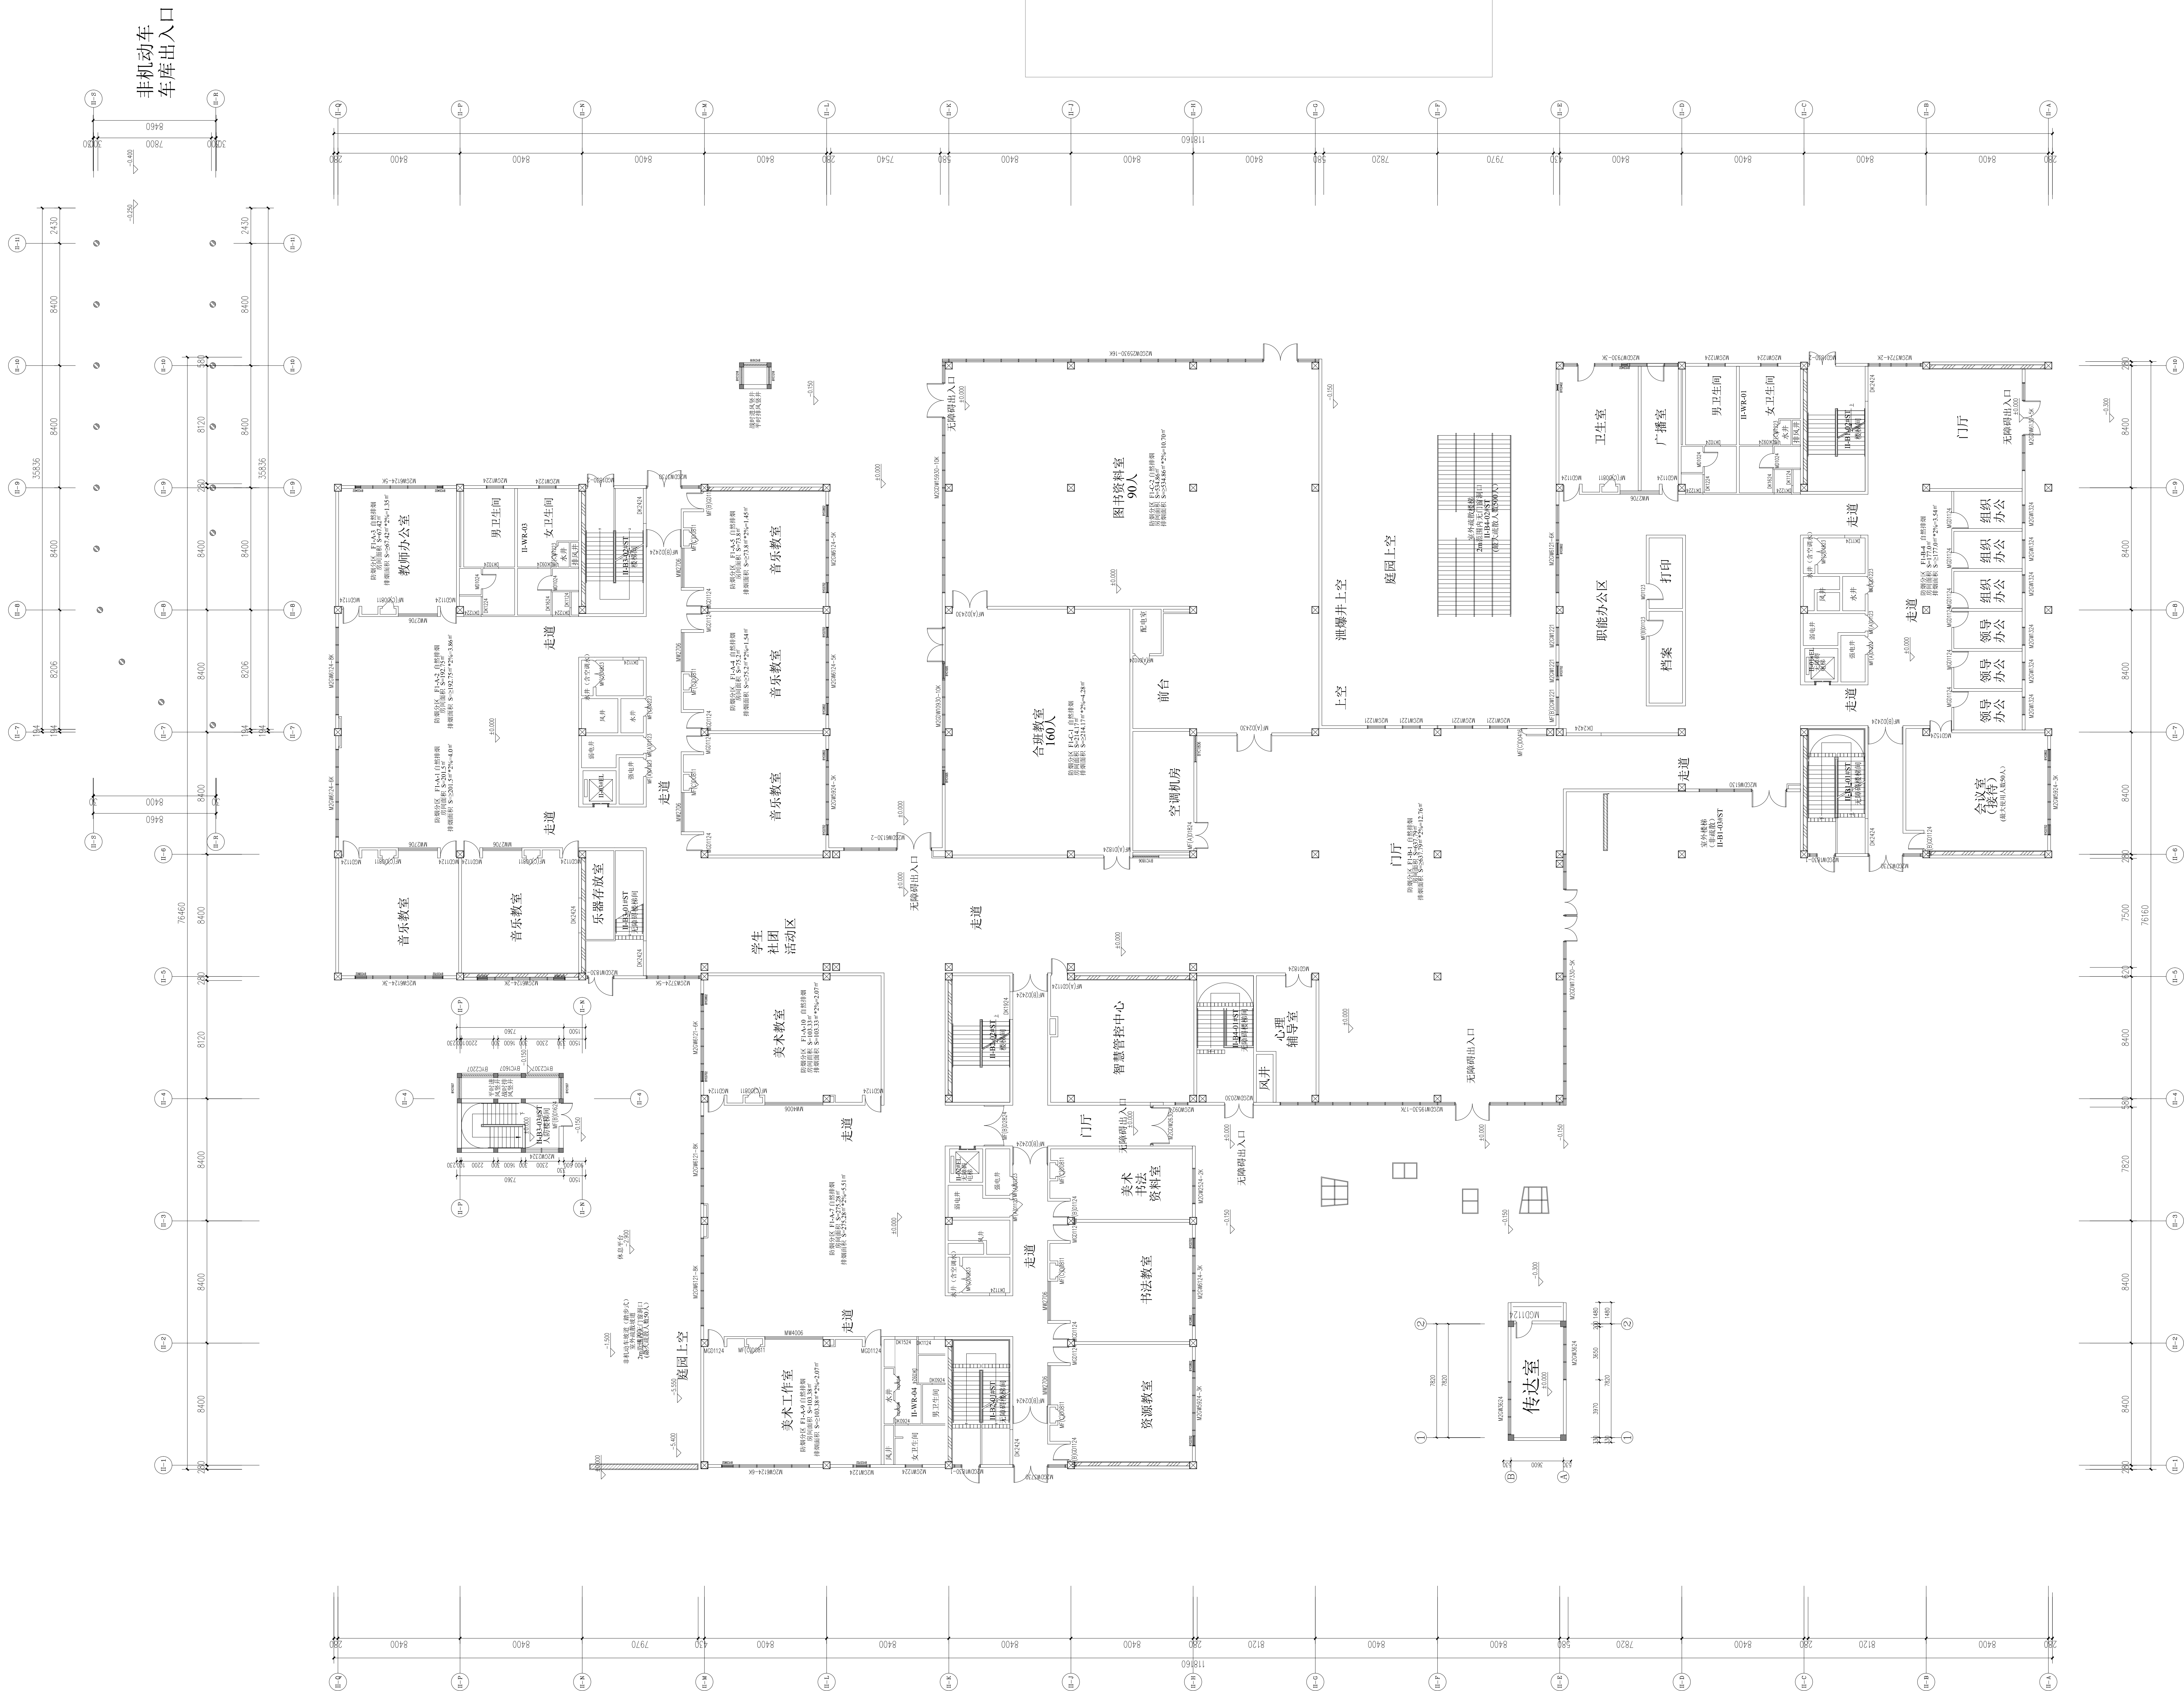

本图纸的著作权及其他相关权益属北京中建设计研究院股份有限公司 (BIAD) 所有, 图中所含的专有技术信息应予保留。未经本公司书面许可, 不得复制本图纸或将信息提供给或露给任何第三方 (本公司与客户另有约定从其约定)。

如盖有交付章的图纸为BIAD正式交付的施工图。

This drawing is the property of BIAD and is not to be reproduced or copied in whole or in part.
It is only to be used for the project and site specifically identified herein and is not to be used on any other

专业设计部门 DEPARTMENT

设计签字	
SIGNATURE	
方案设计师	
ARCHITECT	
设计总工程师	
PROJECT	
专业负责人	
SPECIALIST IN CHARGE	
设计人	
DESIGNED BY	
验证签字	
VERIFICATION	
审核人	
CHECKED BY	
审定人	
APPROVED BY	
会 签	
CONFIRMATION	
暖通专业负责人	
ARDL	
结构专业负责人	
STRUCT.	
给排水专业负责人	
PLUMB.	
暖通空调专业负责人	
HVAC	
电气专业负责人	
ELEC.	

项目名称 PROJECT NAME

项目编号 PROJECT NO.

 DRAWING NAME

设计阶段 PHASE	图号 DRAWING NO.	版本号 EDITION
出图日期 DATE 年 YEAR 月 MONTH 日 DAY		
归档记录 ARCHIVES		

归档记
ARCHIVES