
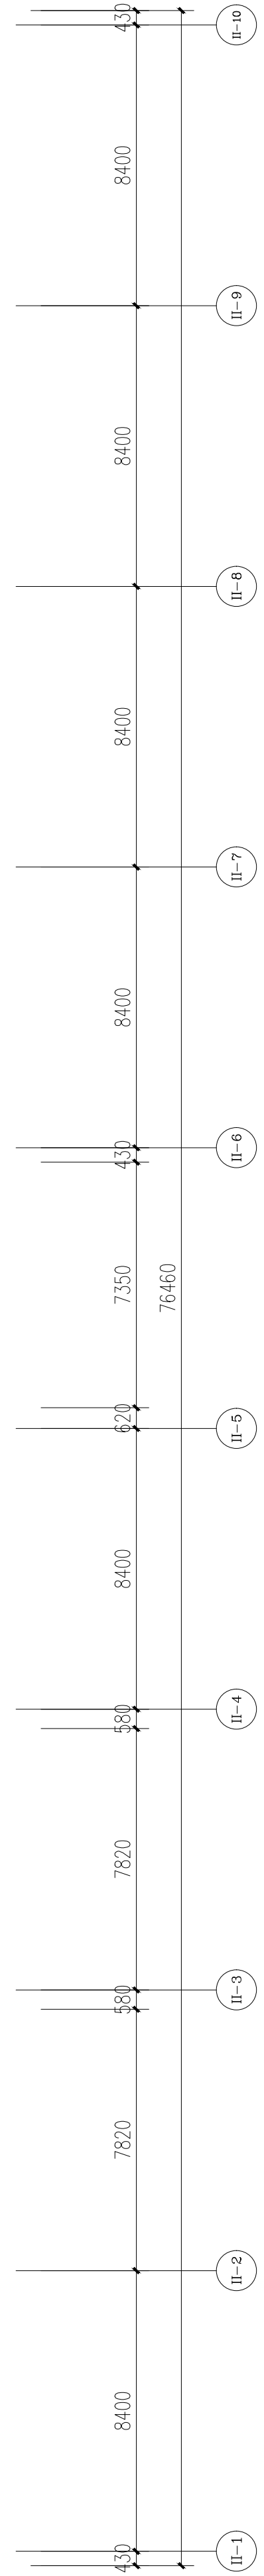


1:300

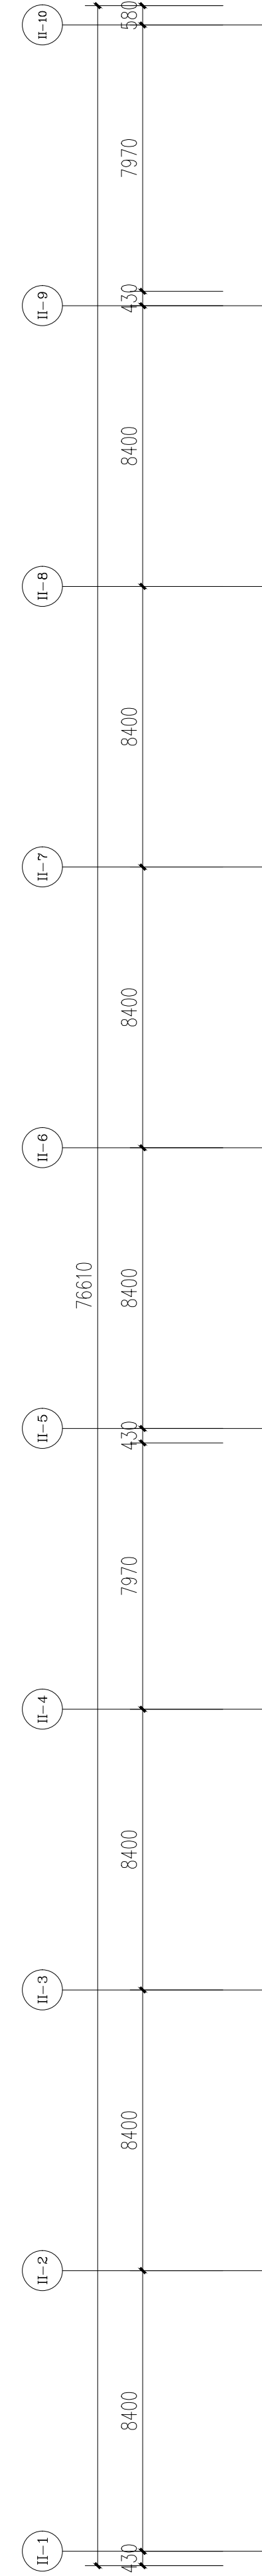

BIAD
北京市建筑设计研究院股份有限公司
BEIJING INSTITUTE OF ARCHITECTURAL DESIGN CO., LTD.

中国 北京 南礼士路62号 100845
NO.62 NANLISHI ROAD, BEIJING, P.R.CHINA
POSTCODE: 100845
TEL: 86-10-88021578
FAX: 86-10-88021570
WEBSITE: WWW.BIAD.COM.CN

本图权的著作权及图形版权归北京中
建设计研究院股份有限公司 (BIAD) 所有。
图中所有的手写标注及信息均由手提供。本图及公
司所有。不得复制或翻印。如有任何复制或翻印
行为, 均须事先取得北京中
建设计研究院股份有限公司 (BIAD) 的书面许可。
如有任何复制或翻印行为, 均须事先取得北京中
建设计研究院股份有限公司 (BIAD) 的书面许可。

专业设计部门 DEPARTMENT

设计签字
SIGNATURE

方案设计人
DESIGNER
设计负责人
DESIGNER
专业负责人
SPECIALIST
设计人
DESIGNER

验证签字
VERIFICATION

审核人
CHECKER
审定人
APPROVED BY

会签
CONFIRMATION

建筑专业负责人
ARCH.
结构专业负责人
STRUCT.
给排水专业负责人
PLUMB.
暖通空调专业负责人
HEATING
电气专业负责人
ELECT.

项目名称 PROJECT NAME

项目编号 PROJECT NO.

图名 DRAWING NAME

设计阶段
PHASE

图号
DRAWING NO.

版本号
VERSION

出图日期
DATE

年 月 日
YEAR MONTH DAY

修改记录
MODIFICATION